


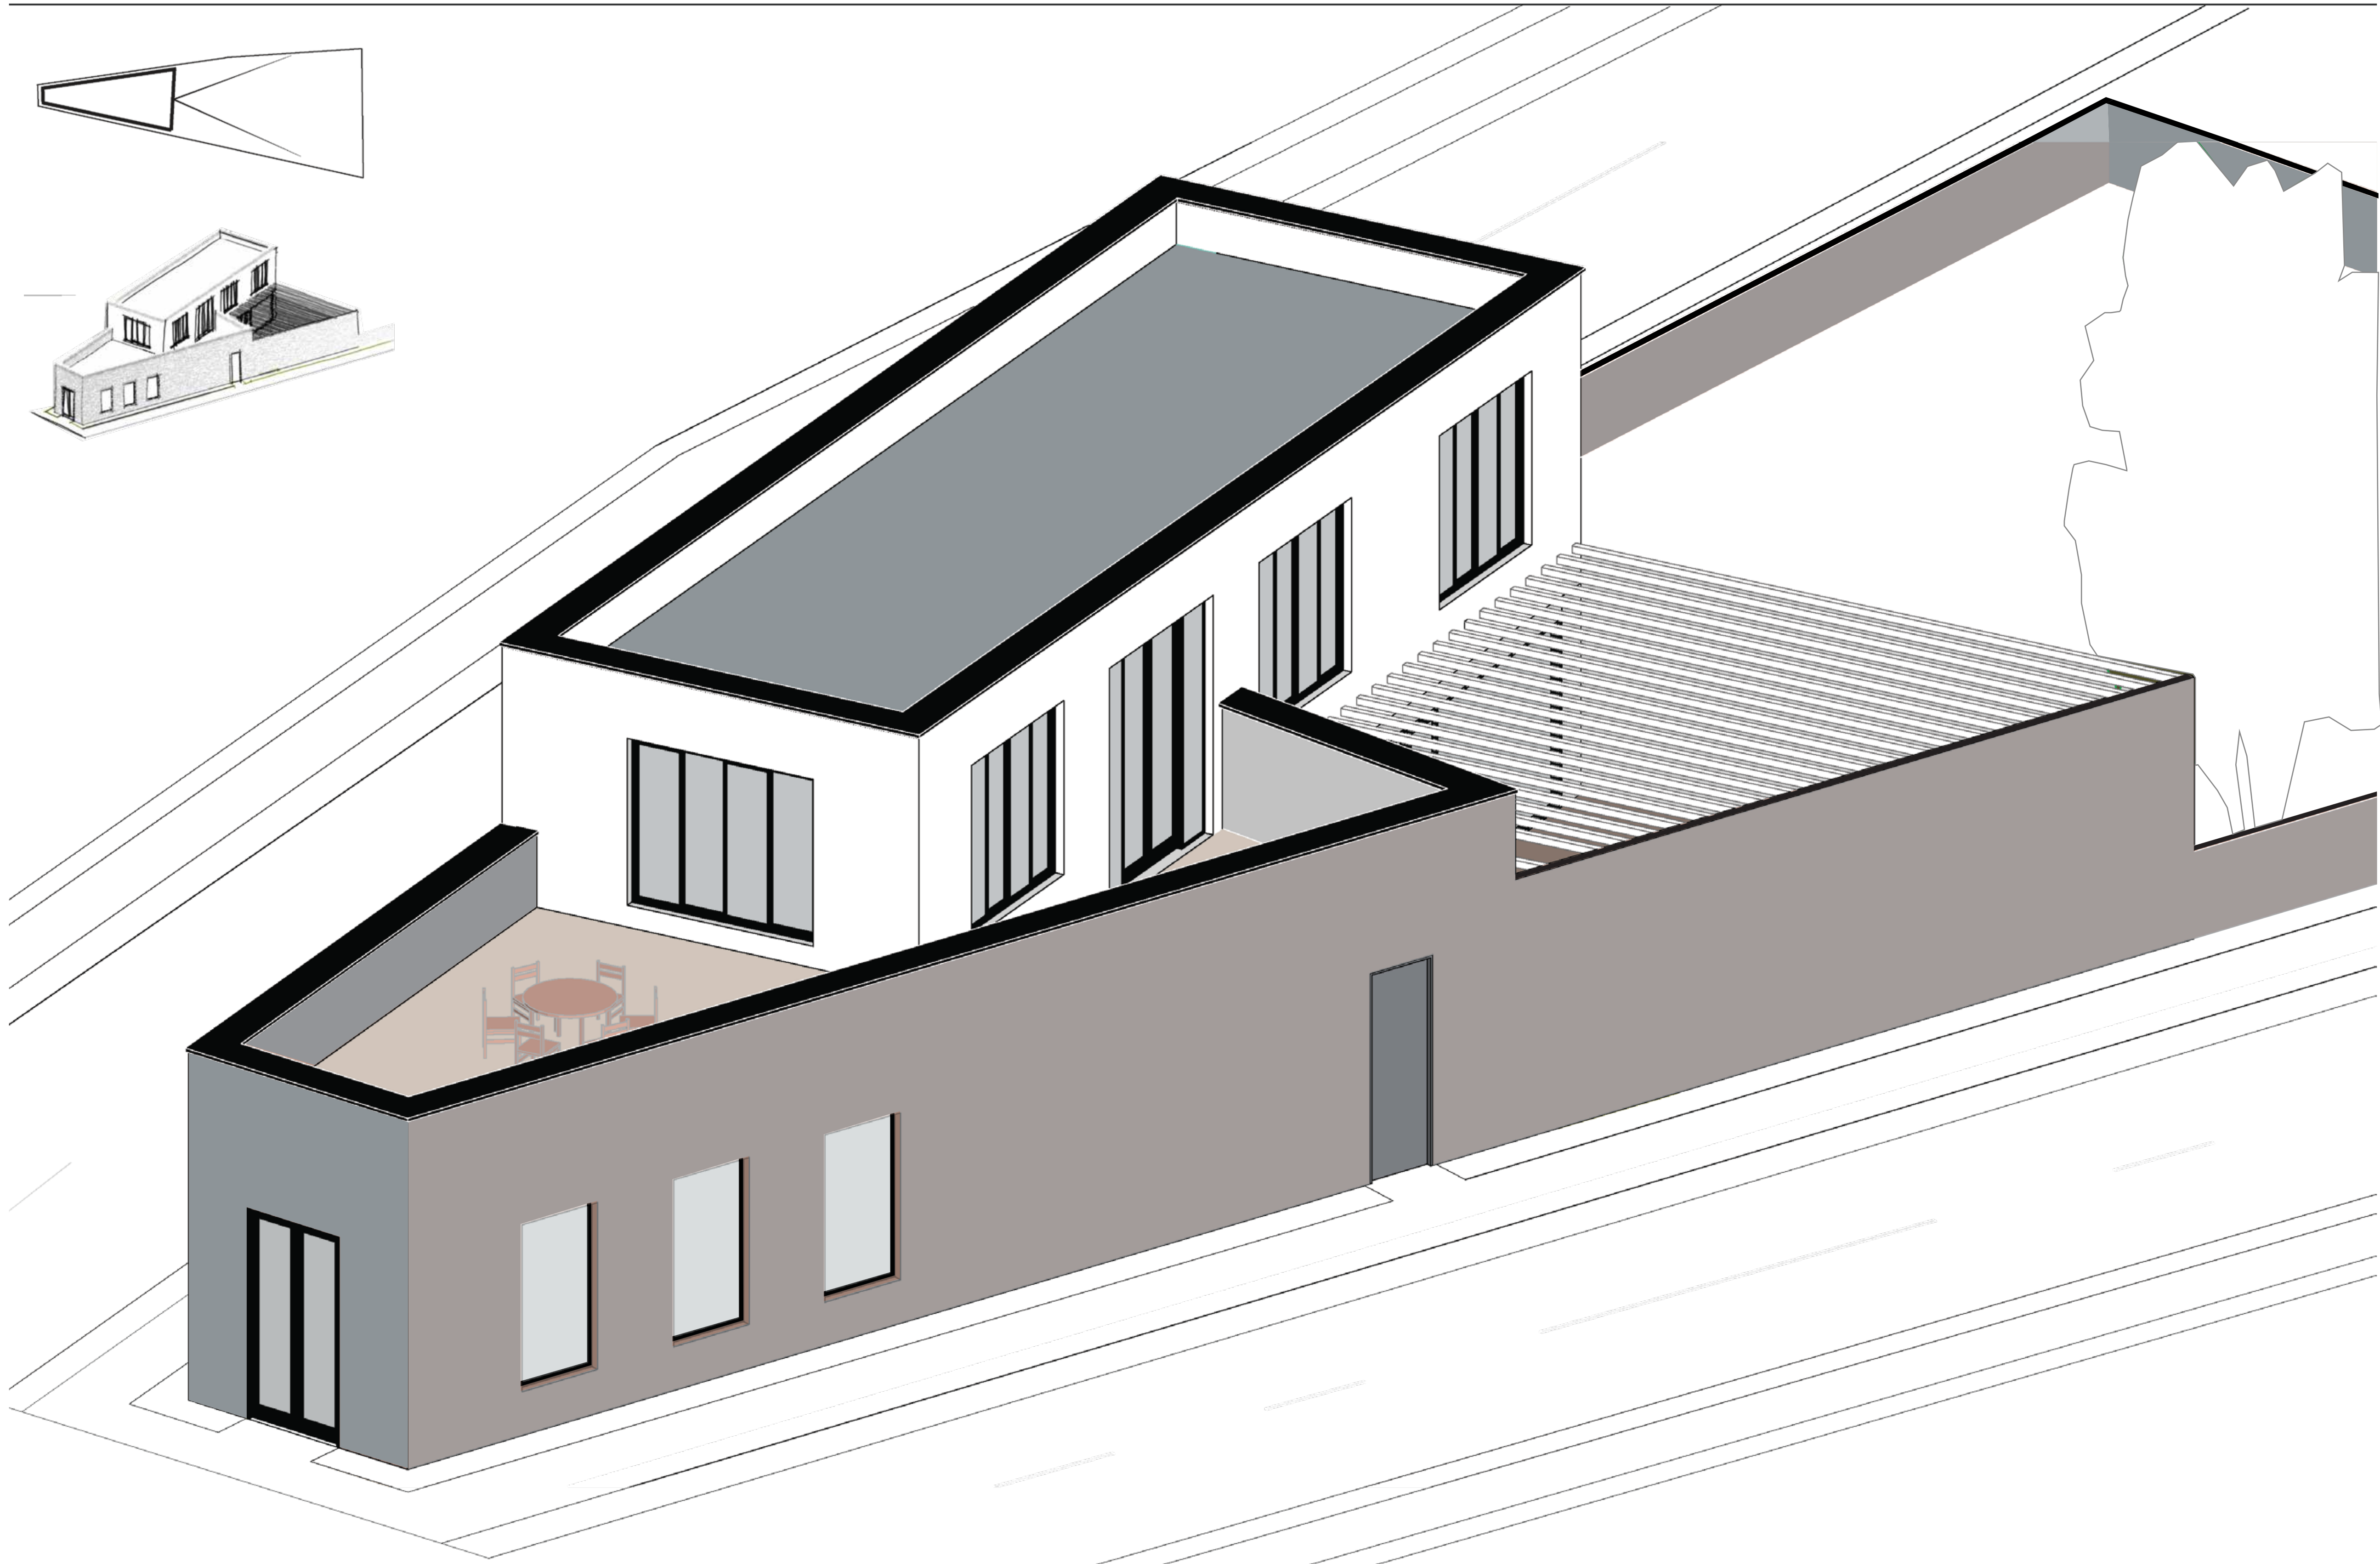

LOCATION: Szőny, Kossuth utca 43:


This property is situated in the heart of the village, providing a unique opportunity to contribute to the local community's vibrancy. By incorporating a shop on the ground floor, the design can create a lively and engaging space that serves both residents and visitors.

CONCEPT:



The vision for this project is a corner house that not only serves as a comfortable residence but also includes a ground-floor shop. This dual-purpose design aims to enhance the social and economic activity in the area, making the most of its central location.

SITE LAYOUT:

The design of the house should be thoughtfully integrated into the existing site layout, ensuring it complements the surrounding environment and maximizes the available space.

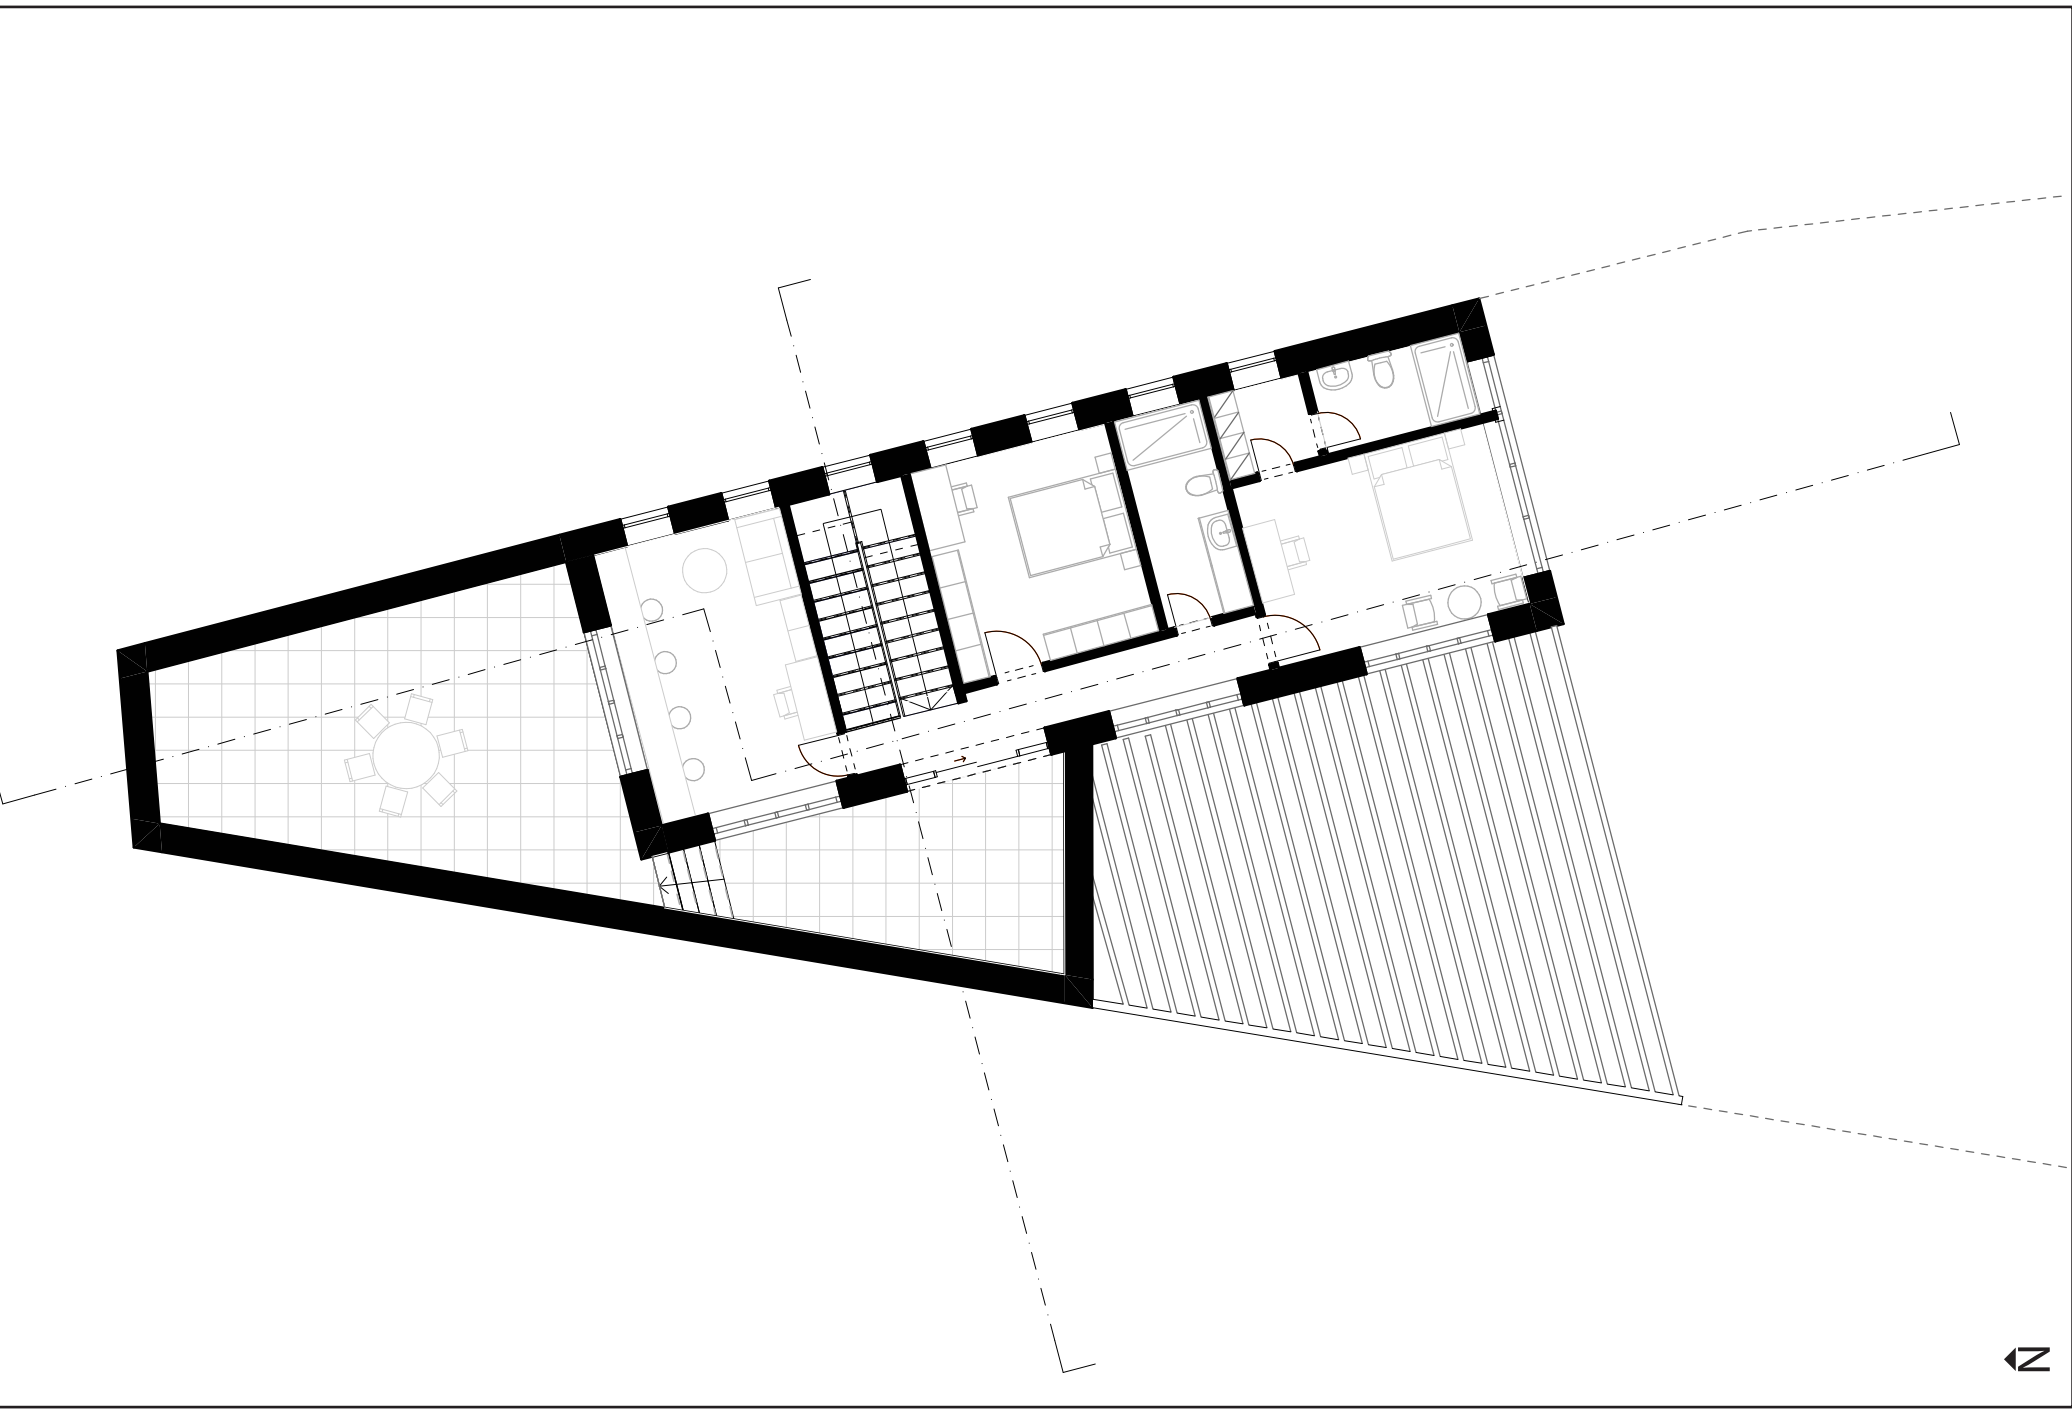

FIRST FLOOR PLAN

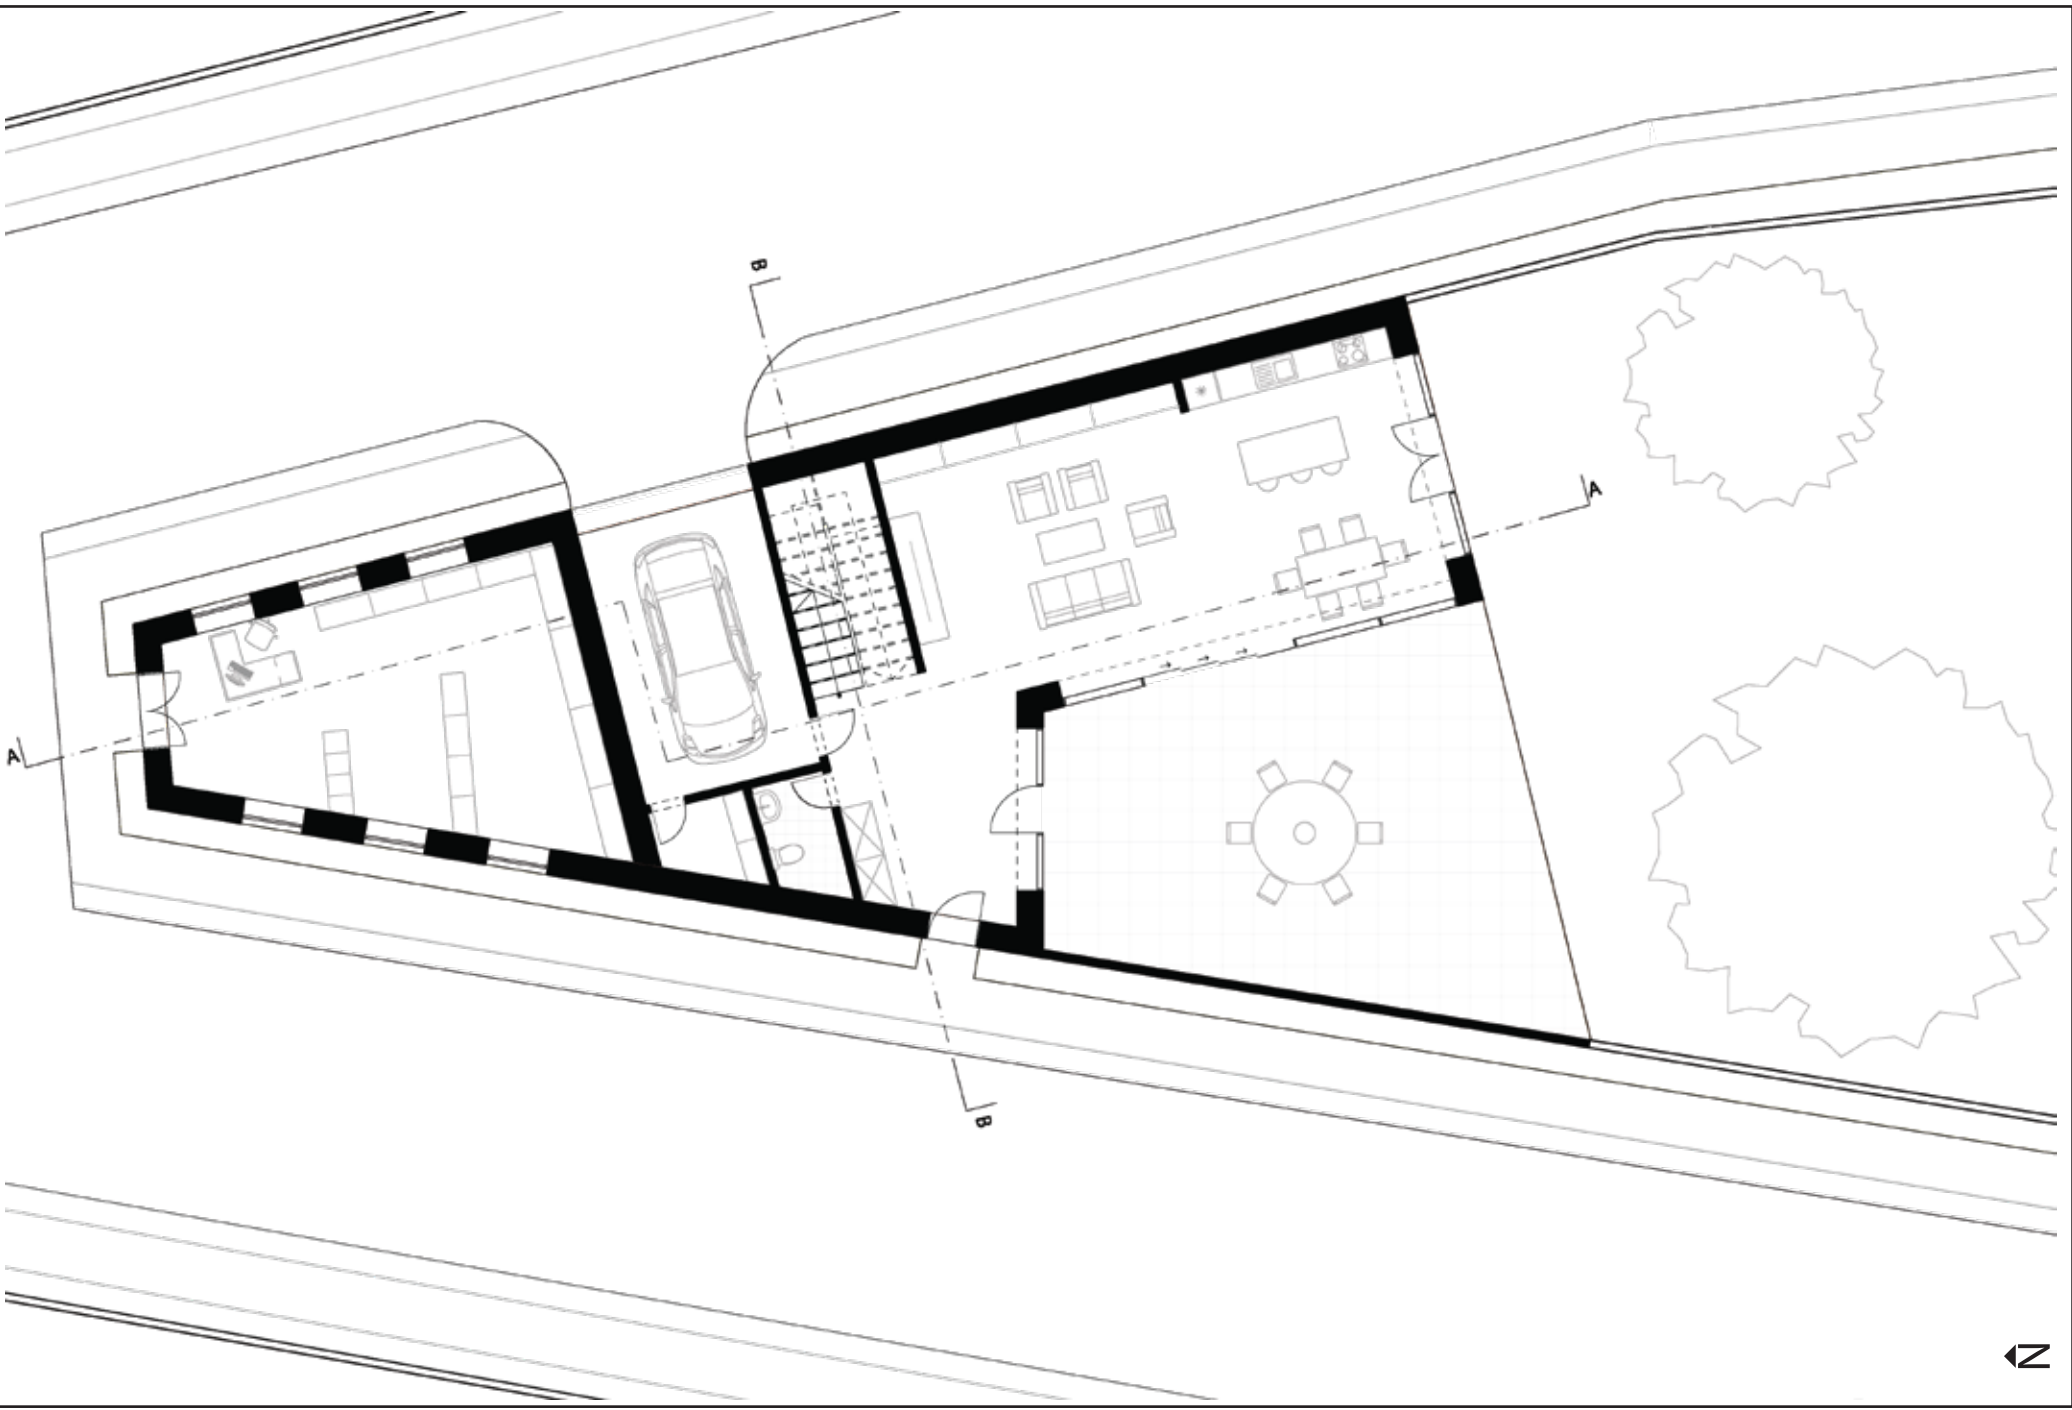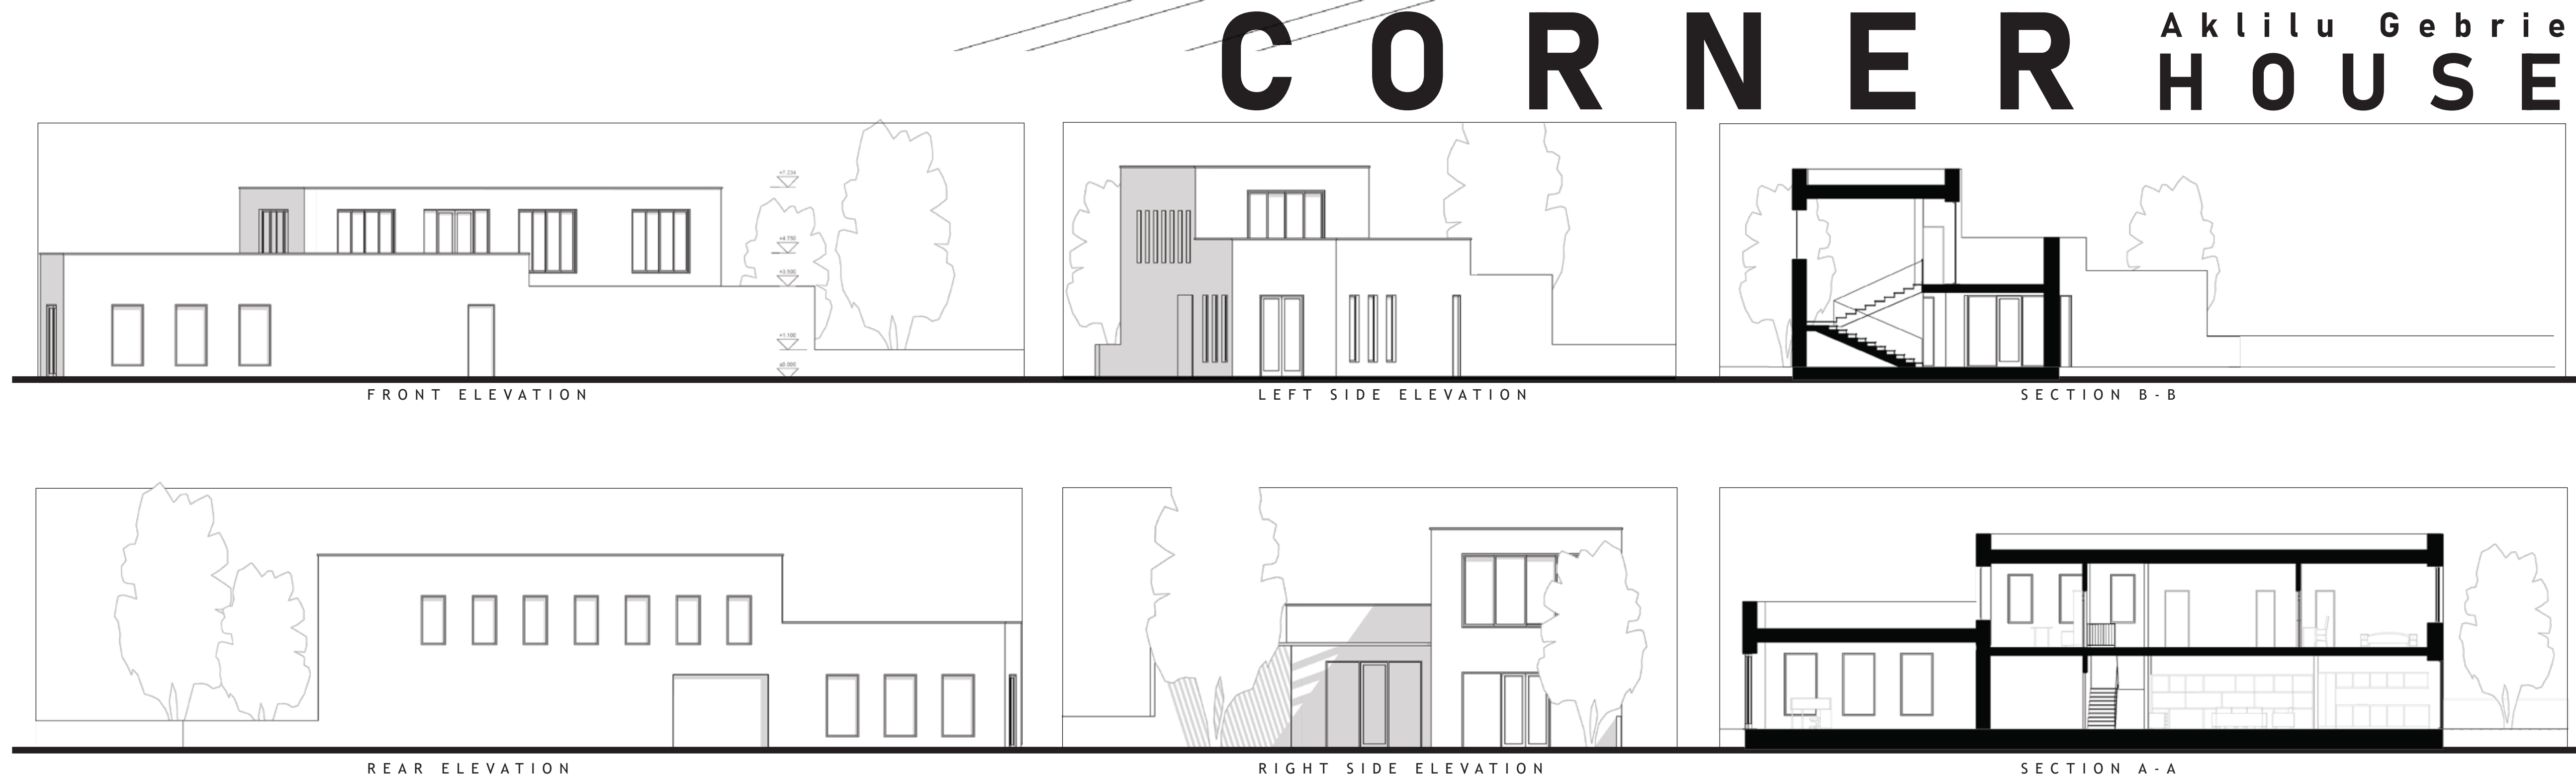

GROUND FLOOR PLAN